



DEFENSE LOGISTICS AGENCY
LAND AND MARITIME
P.O. BOX 3990
COLUMBUS, OHIO 43218-3990

DLA LAND AND MARITIME-VAI

18 August 2025

MEMORANDUM FOR MILITARY/INDUSTRY DISTRIBUTION

SUBJECT: Initial Drafts of various MIL-DTL-38999 Slash Sheets
(see table below for details).

These initial drafts for these subject documents are now available for viewing and downloading from the DLA Land and Maritime-VA Web site:

<https://landandmaritimeapps.dla.mil/Programs/MilSpec/DocSearch.aspx>

Initial Draft	Title	Project Number
MIL-DTL-38999/10C	Connectors, Electrical, Circular, Receptacle, Dummy Stowage, Bayonet Coupling, (MIL-DTL-27599, Series II and MIL-DTL-38999, Series II)	5935-2025-086
MIL-DTL-38999/20J	Connectors, Electrical, Circular, Receptacle, Threaded, Wall Mounting Flange, Removable Crimp Contacts, Series III, Metric	5935-2025-087
MIL-DTL-38999/21D	Connectors, Electrical, Circular, Threaded, Receptacle, Box Mounting Flange, Hermetic, Hermetic Solder Contacts, Series III, Metric	5935-2025-088
MIL-DTL-38999/22K	Connectors, Electrical, Circular, Receptacle, Threaded, Dummy Stowage, Series III, Metric	5935-2025-089
MIL-DTL-38999/23D	Connectors, Electrical, Circular, Threaded, Receptacle, Jam-Nut Mounting, Hermetic, Hermetic Solder Contacts, Series III, Metric	5935-2025-092
MIL-DTL-38999/24K	Connectors, Electrical, Circular, Receptacle, Threaded, Jam-Nut Mounting, Removable Crimp Contacts, Series III, Metric	5935-2025-093
MIL-DTL-38999/25D	Connector, Electrical, Circular, Threaded, Receptacle, Solder Mounting, Hermetic, Solder Contacts, Series III, Metric	5935-2025-094
MIL-DTL-38999/26H	Connectors, Electrical, Plug, Circular, Threaded, Straight, Removable Crimp Contacts, Series III, Metric	5935-2025-095
MIL-DTL-38999/27D	Connectors, Electrical, Circular, Threaded, Receptacle, Weld Mounting, Hermetic, Hermetic Solder Contacts, Series III, Metric	5935-2025-096
MIL-DTL-38999/28J	Connectors, Electrical, Circular, Nut, Hexagon, Connector Mounting, Series III and IV, Metric	5935-2025-097
MIL-DTL-38999/29D	Connectors, Electrical, Circular, Threaded, Plug, Lanyard Release, Fail-Safe, Removable Crimp Contacts, Pins, Series III, Metric	5935-2025-098
MIL-DTL-38999/30D	Connectors, Electrical, Circular, Threaded, Plug, Lanyard Release, Fail-Safe, Removable Crimp Contacts, Sockets, Series III, Metric	5935-2025-099

Major changes to these documents include removing dimensional equivalents.

Concurrence or comments are required at this Center within 30 days. Late comments will be held for the next coordination of the document. Comments from military departments must be identified as either "Essential" or "Suggested". Essential comments must be justified with supporting data. Military review activities should forward comments to their custodians of this office, as applicable, in sufficient time to allow for consolidating the department reply. Lack of response to this draft will be construed as concurrence.

If these documents are of interest to you, please provide your comments or suggested changes. The point of contact for this document is Mr. Bender, phone number 614-692-9185, facsimile transmission, 614-692-6939, e-mail Jacob.Bender@dla.mil or may be mailed via the US Postal Service to DLA LAND AND MARITIME, ATTN: VAI (Attention: Jacob Bender), P.O. Box 3990, Columbus, OH 43218-3990.

Sincerely,

/SIGNED/

ERIC CANDELARIA
Acting Chief,
Interconnection Branch

CC: David Devine, Robert Schoening, Alan Drais, Eddie Shen, Deborah Thompson

Note: This initial draft, dated August 22, 2025, prepared by DLA-CC has not been approved and is subject to modification.
DO NOT USE FOR ACQUISITION PURPOSES.
(Project: 5935-2025-086)

INCH - POUND

MIL-DTL-38999/10C
DRAFT
SUPERSEDING
MIL-DTL-38999/10B
w/AMENDMENT 2
11 August 2022

DETAIL SPECIFICATION SHEET

CONNECTORS, ELECTRICAL, CIRCULAR, RECEPTACLE, DUMMY STOWAGE,
BAYONET COUPLING, (MIL-DTL-27599, SERIES II AND MIL-DTL-38999, SERIES II)

This specification is approved for use by all Departments
and Agencies of the Department of Defense.

The requirements for acquiring the product described herein
shall consist of this specification sheet and MIL-DTL-38999.


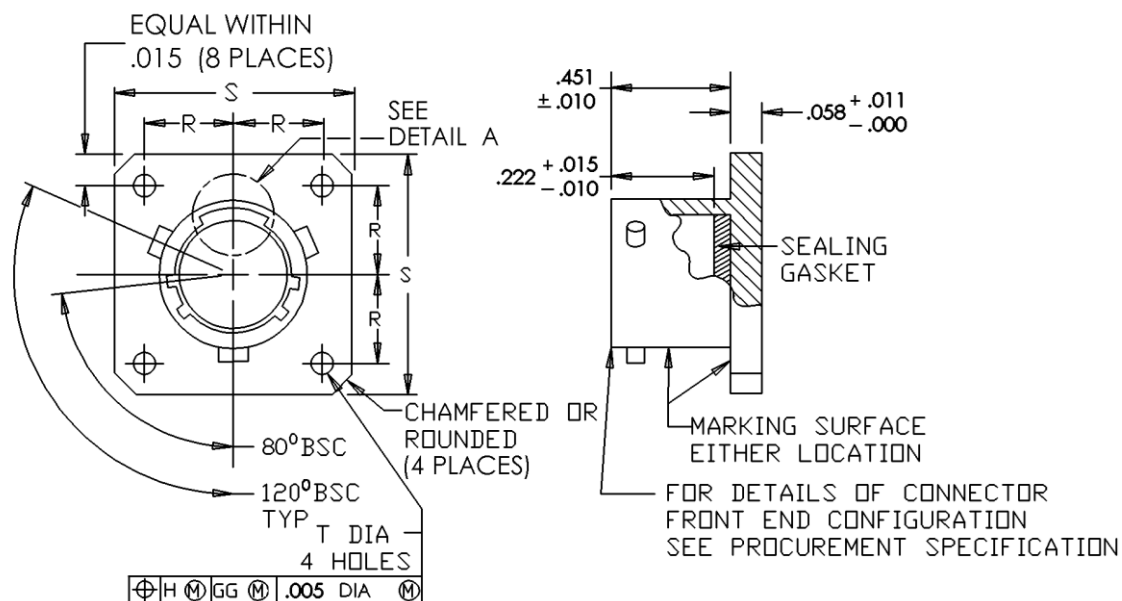


FIGURE 1. Dummy receptacle, finish B.



MIL-DTL-38999/10C
DRAFT DATED 22 AUGUST 2025

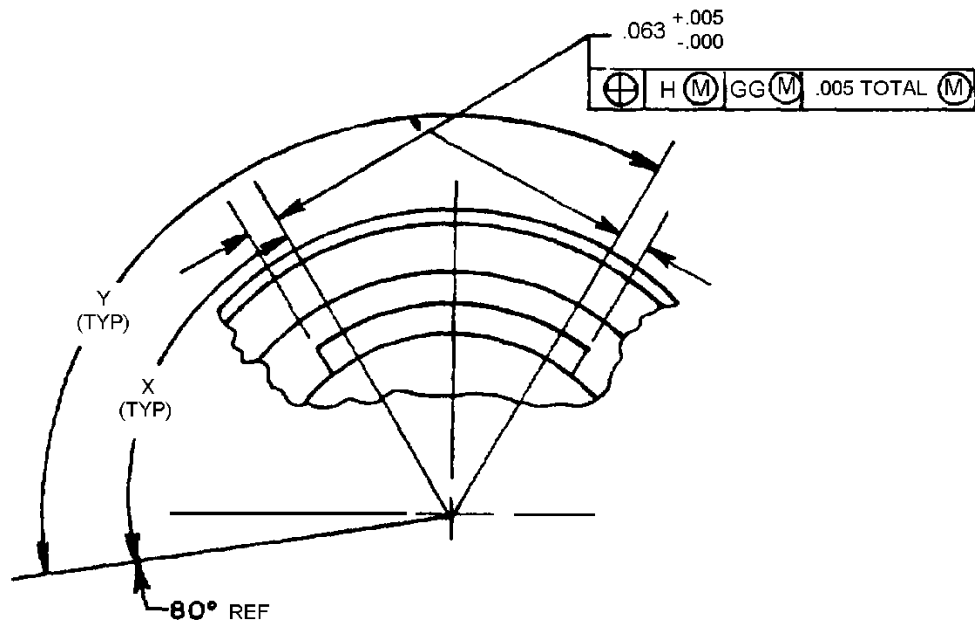

DETAIL A

Dimensions					
Shell size	R BSC	S max	T dia +.010 -.005	X (TYP)	Y (TYP)
8	.297	.828	.120	82°	118°
10	.3595	.954		72°	128°
12	.406	1.047		68°	132°
14	.453	1.141		66°	134°
16	.4845	1.234		70°	130°
18	.531	1.328		70°	130°
20	.578	1.453		70°	130°
22	.625	1.578	.147	74°	126°
24	.6875	1.703		74°	126°

FIGURE 1. Dummy receptacle, finish B - Continued.

MIL-DTL-38999/10C
DRAFT DATED 22 AUGUST 2025

NOTES:

1. Dimensions are in inches.
2. The gage features for GG shall be .010 inch (.25 mm) smaller than the MMC size at basic location.
3. Flange is solid.
4. Dummy receptacles are used when unmated plugs must be protected.

FIGURE 1. Dummy receptacle, finish B - Continued.

REQUIREMENTS:

Dimensions and configuration: See figure 1.

Interface dimensions shall conform to MIL-DTL-38999, except as noted.

Material:

Shell: Aluminum alloy as specified in MIL-DTL-38999 with finish B.

Sealing gasket: Non-corrosive silicone or fluorosilicone elastomer.

This receptacle mates with MS27473, MS27480, MS27484 and MS27500.

Fits all polarization positions.

Part or Identifying Number (PIN) example:

M38999/10 - 10 B

<u>M38999/10</u>	Specification sheet number
<u>10</u>	Shell size
<u>B</u>	Finish

NOTE: The term PIN is equivalent to the term (part number, identification number, and type designator) which was previously used in this specification. In the PIN, a dash symbol ("-") shall be placed between the specification sheet number and shell size.

Qualification:

Qualification shall consist of the dynamic salt spray test, altitude immersion, coupling torque, coupling pin strength, and visual and mechanical inspection as specified in MIL-DTL-38999, conducted on two samples of each shell size.

Changes from previous issue. Marginal notations are not used in this revision to identify changes with respect to the previous issue due to the extent of the changes.

Referenced documents. In addition to MIL-DTL-38999, this document references the following:

MIL-DTL-27599
MS27473
MS27480
MS27484
MS27500

MIL-DTL-38999/10C
DRAFT DATED 22 AUGUST 2025

CONCLUDING MATERIAL

Custodians:

Army - CR
Navy - AS
Air Force - 85
DLA - CC

Preparing activity:
DLA - CC

(Project 5935-2025-086)

Review activities:

Army - AR, MI
Navy - EC, MC, OS
Air Force – 19

NOTE: The activities listed above were interested in this document as of the date of this document. Since organizations and responsibilities can change, you should verify the currency of the information above using the ASSIST Online database at <https://assist.dla.mil>.